

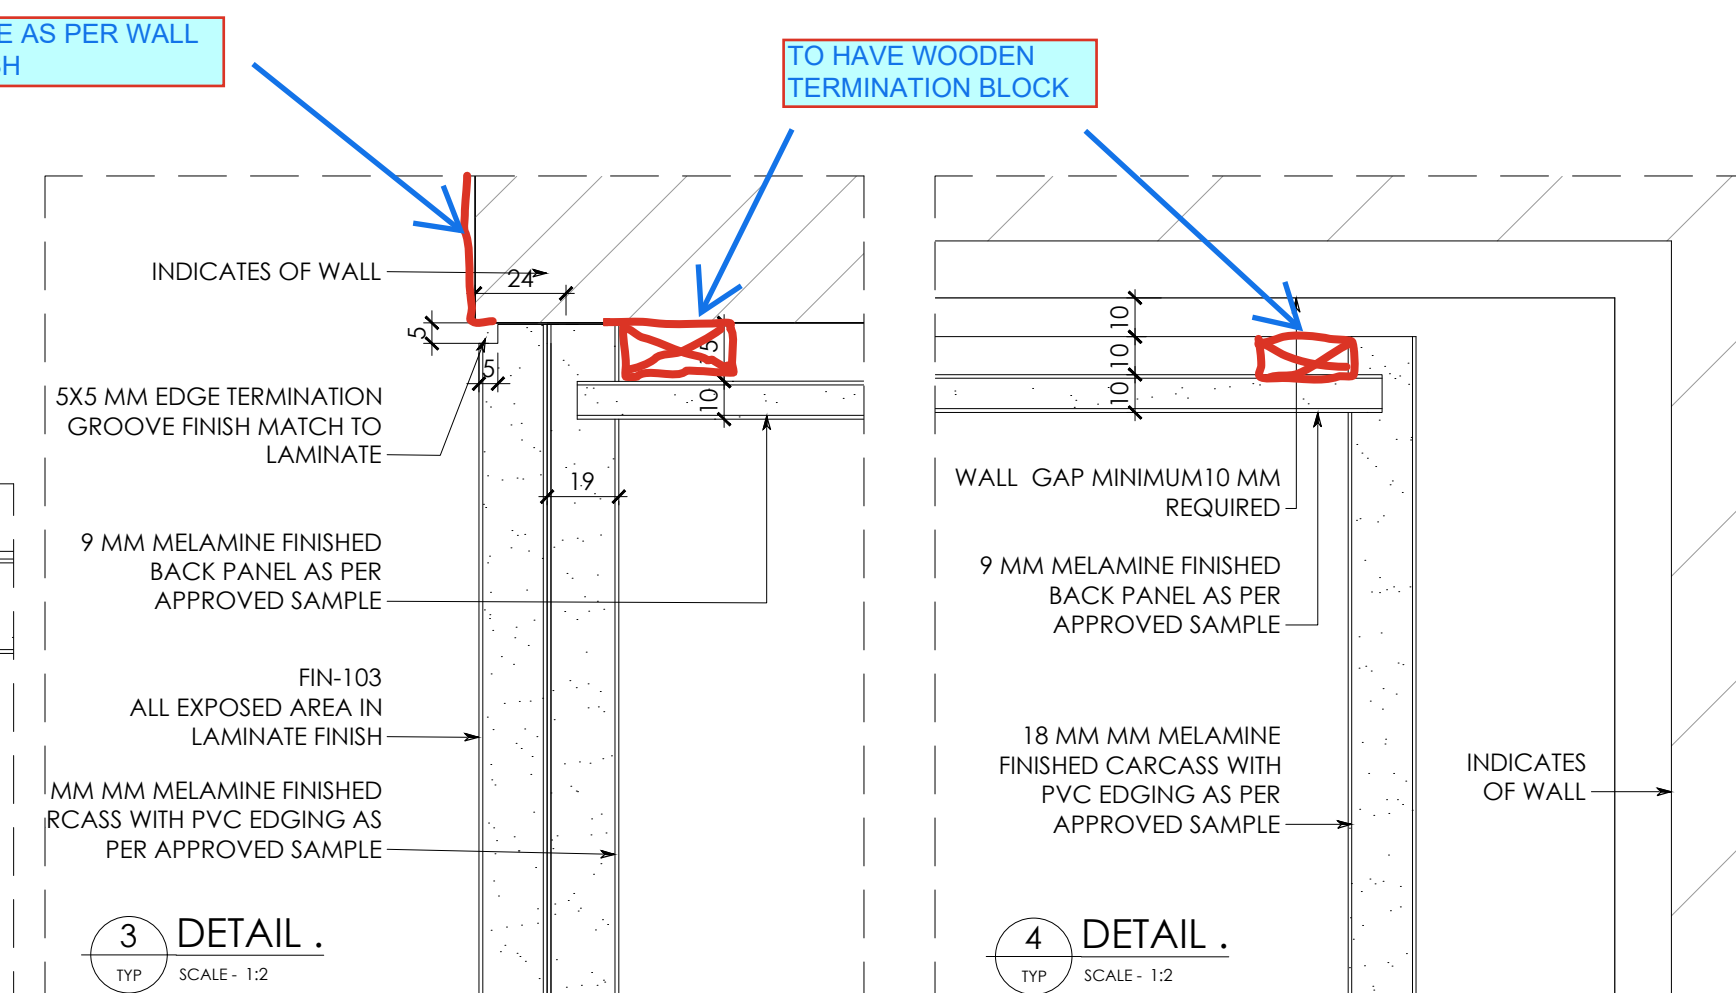
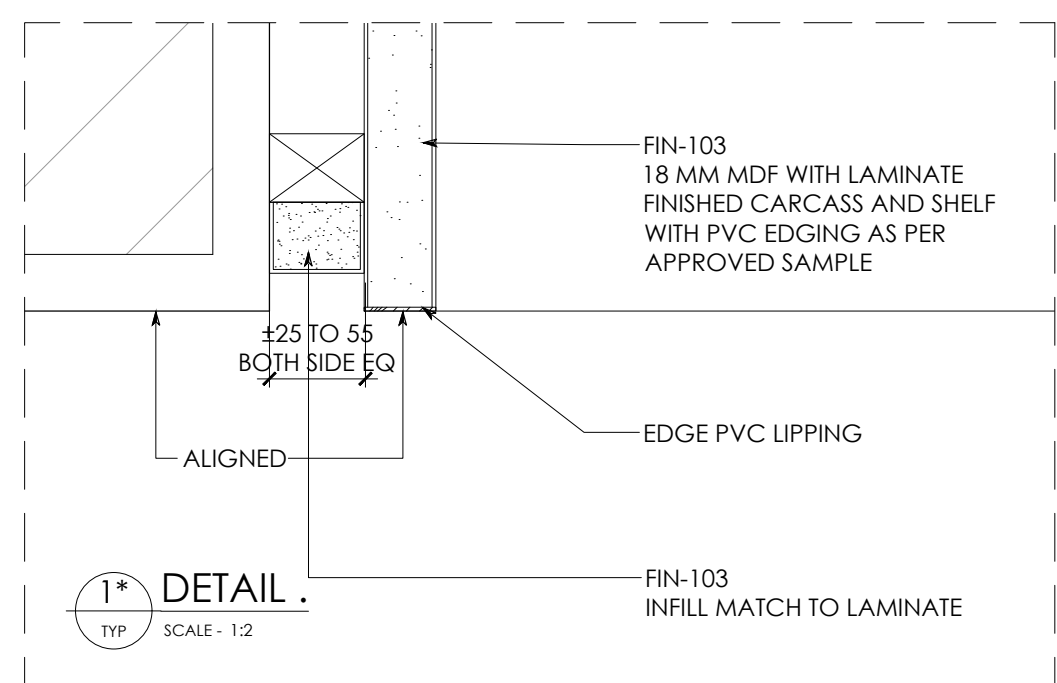
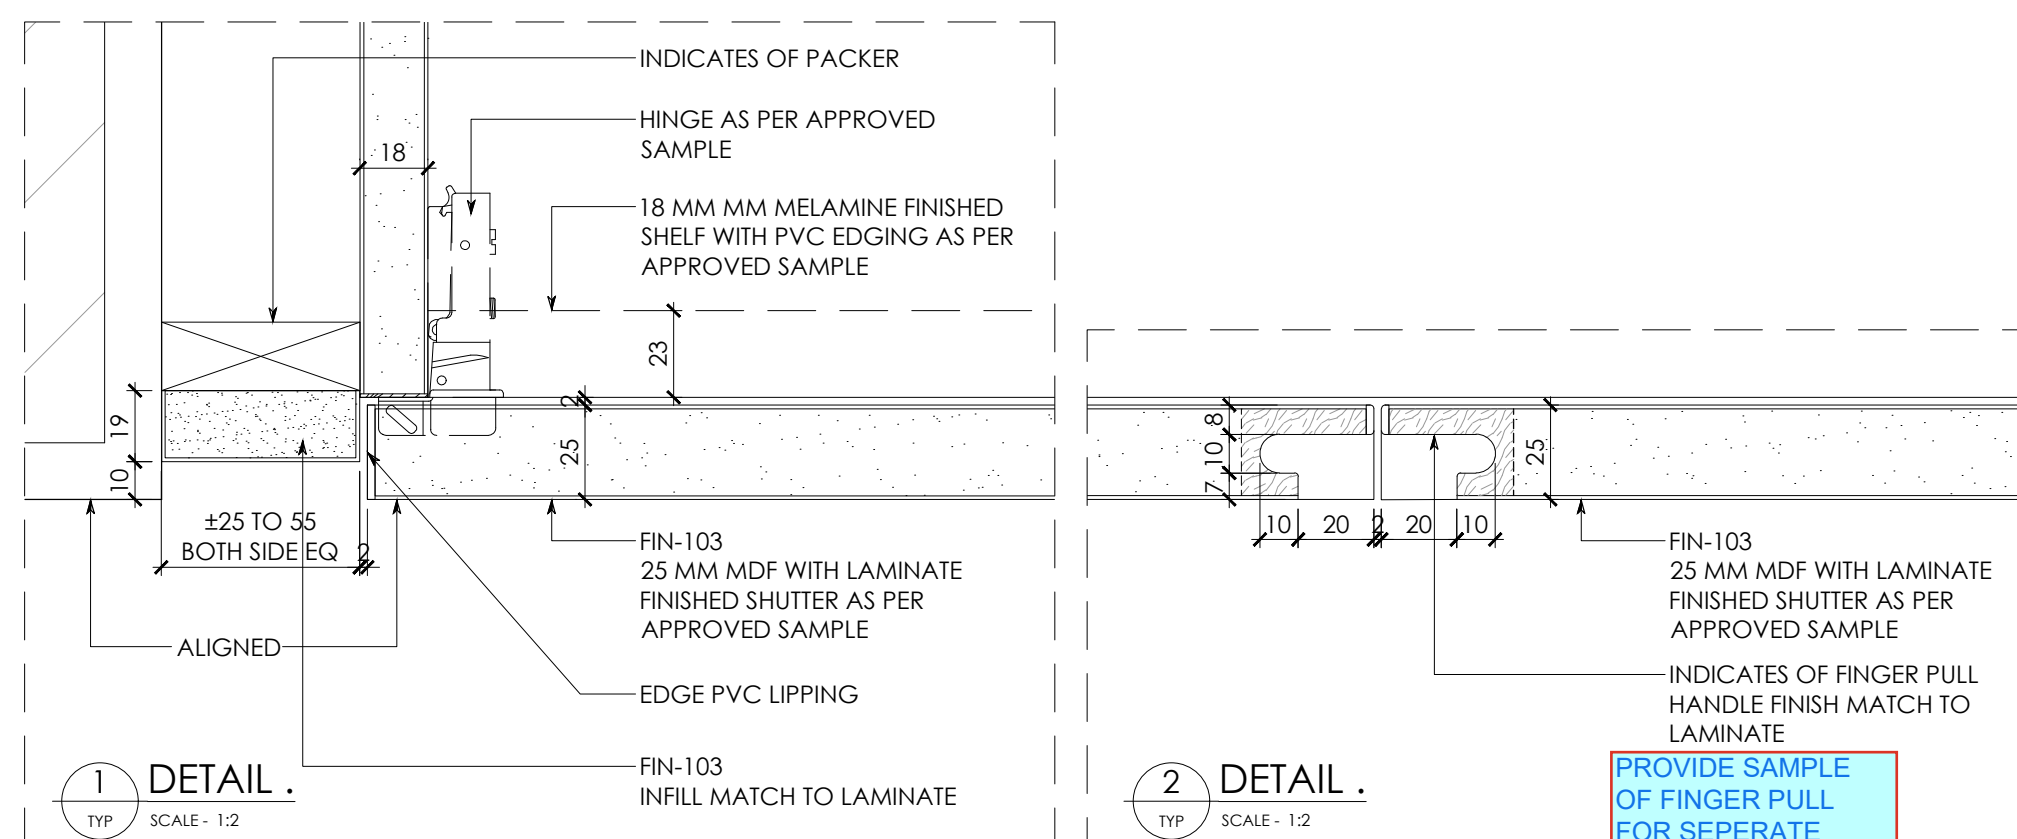
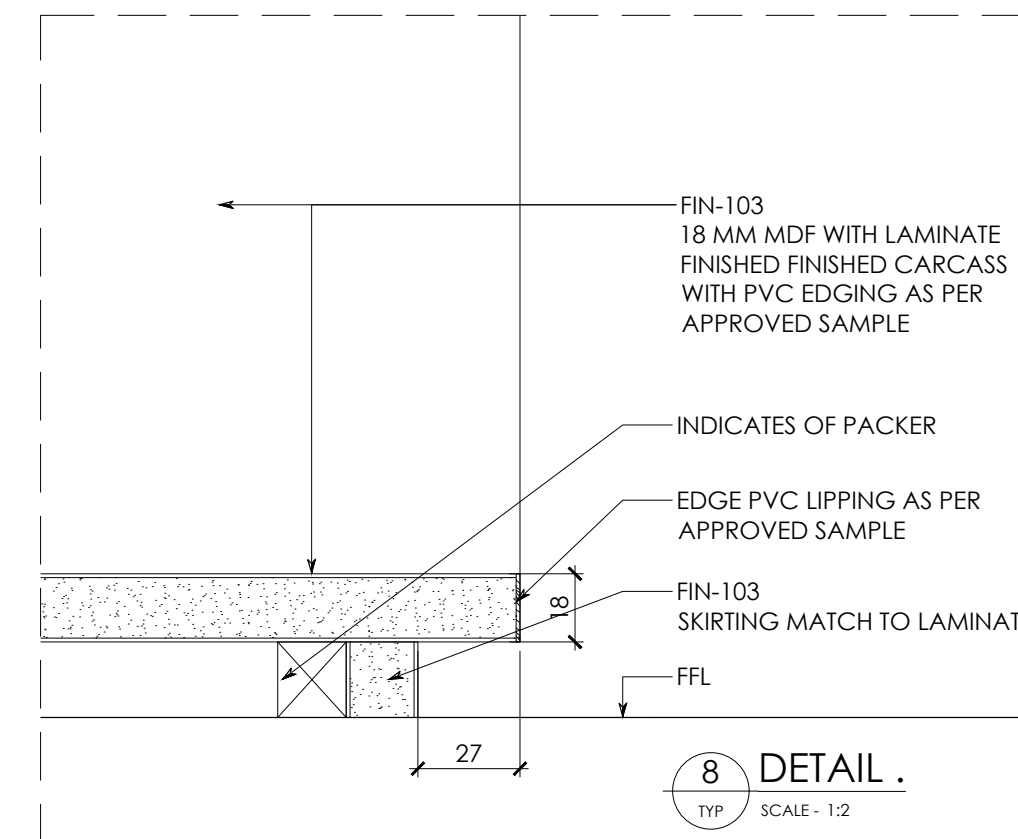
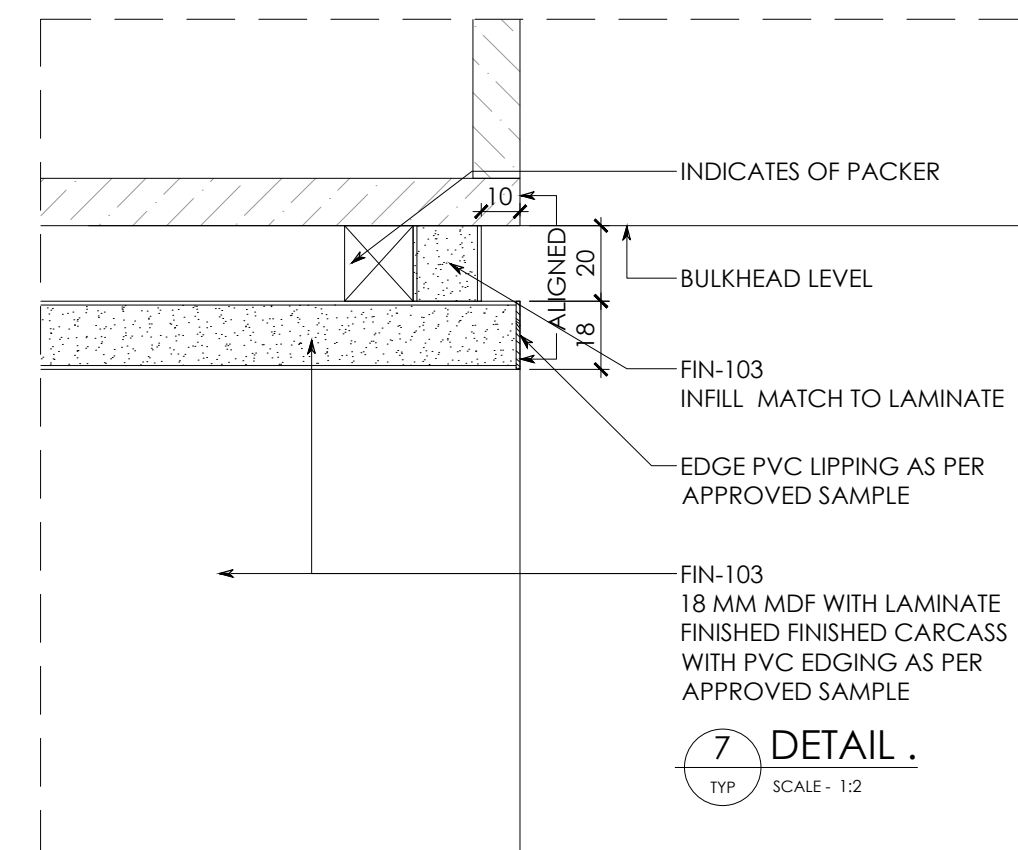
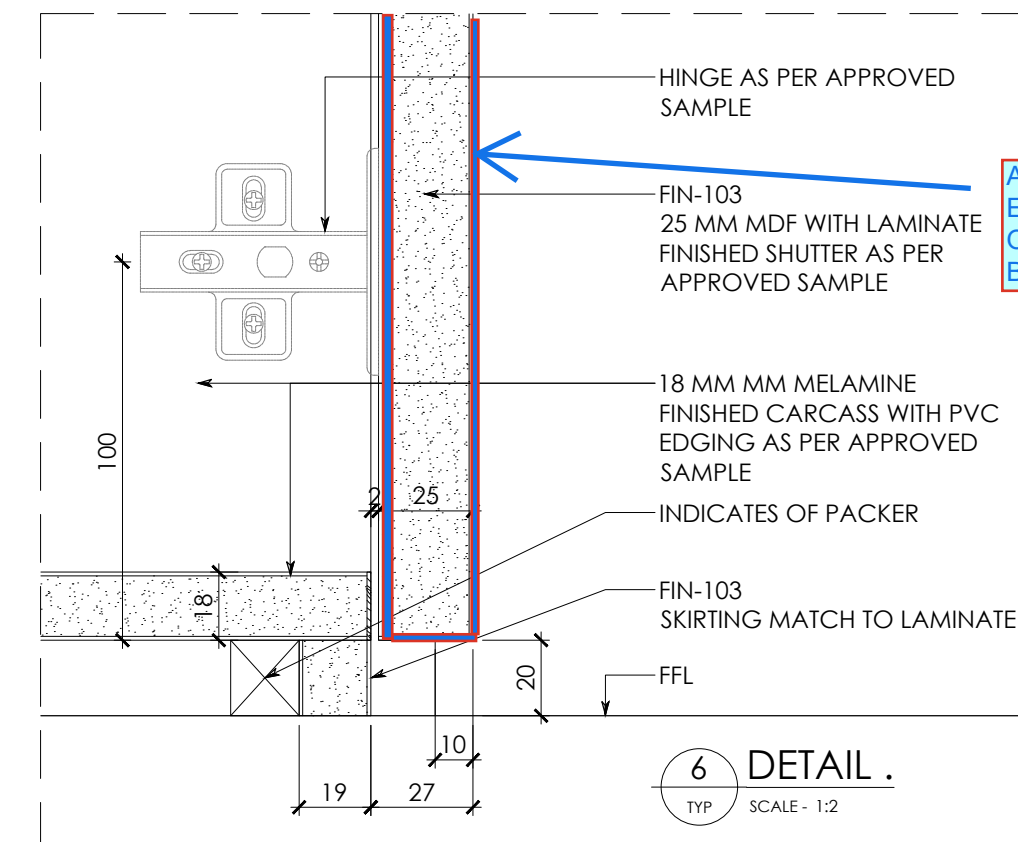
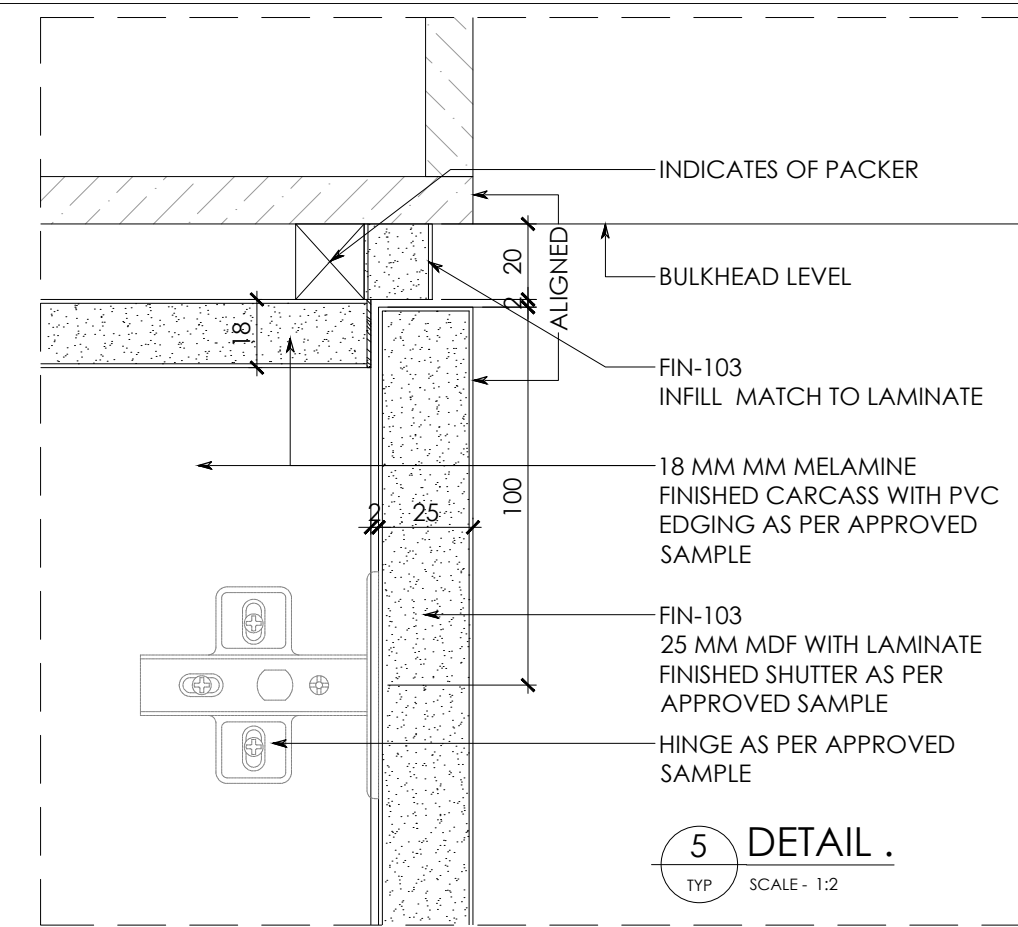


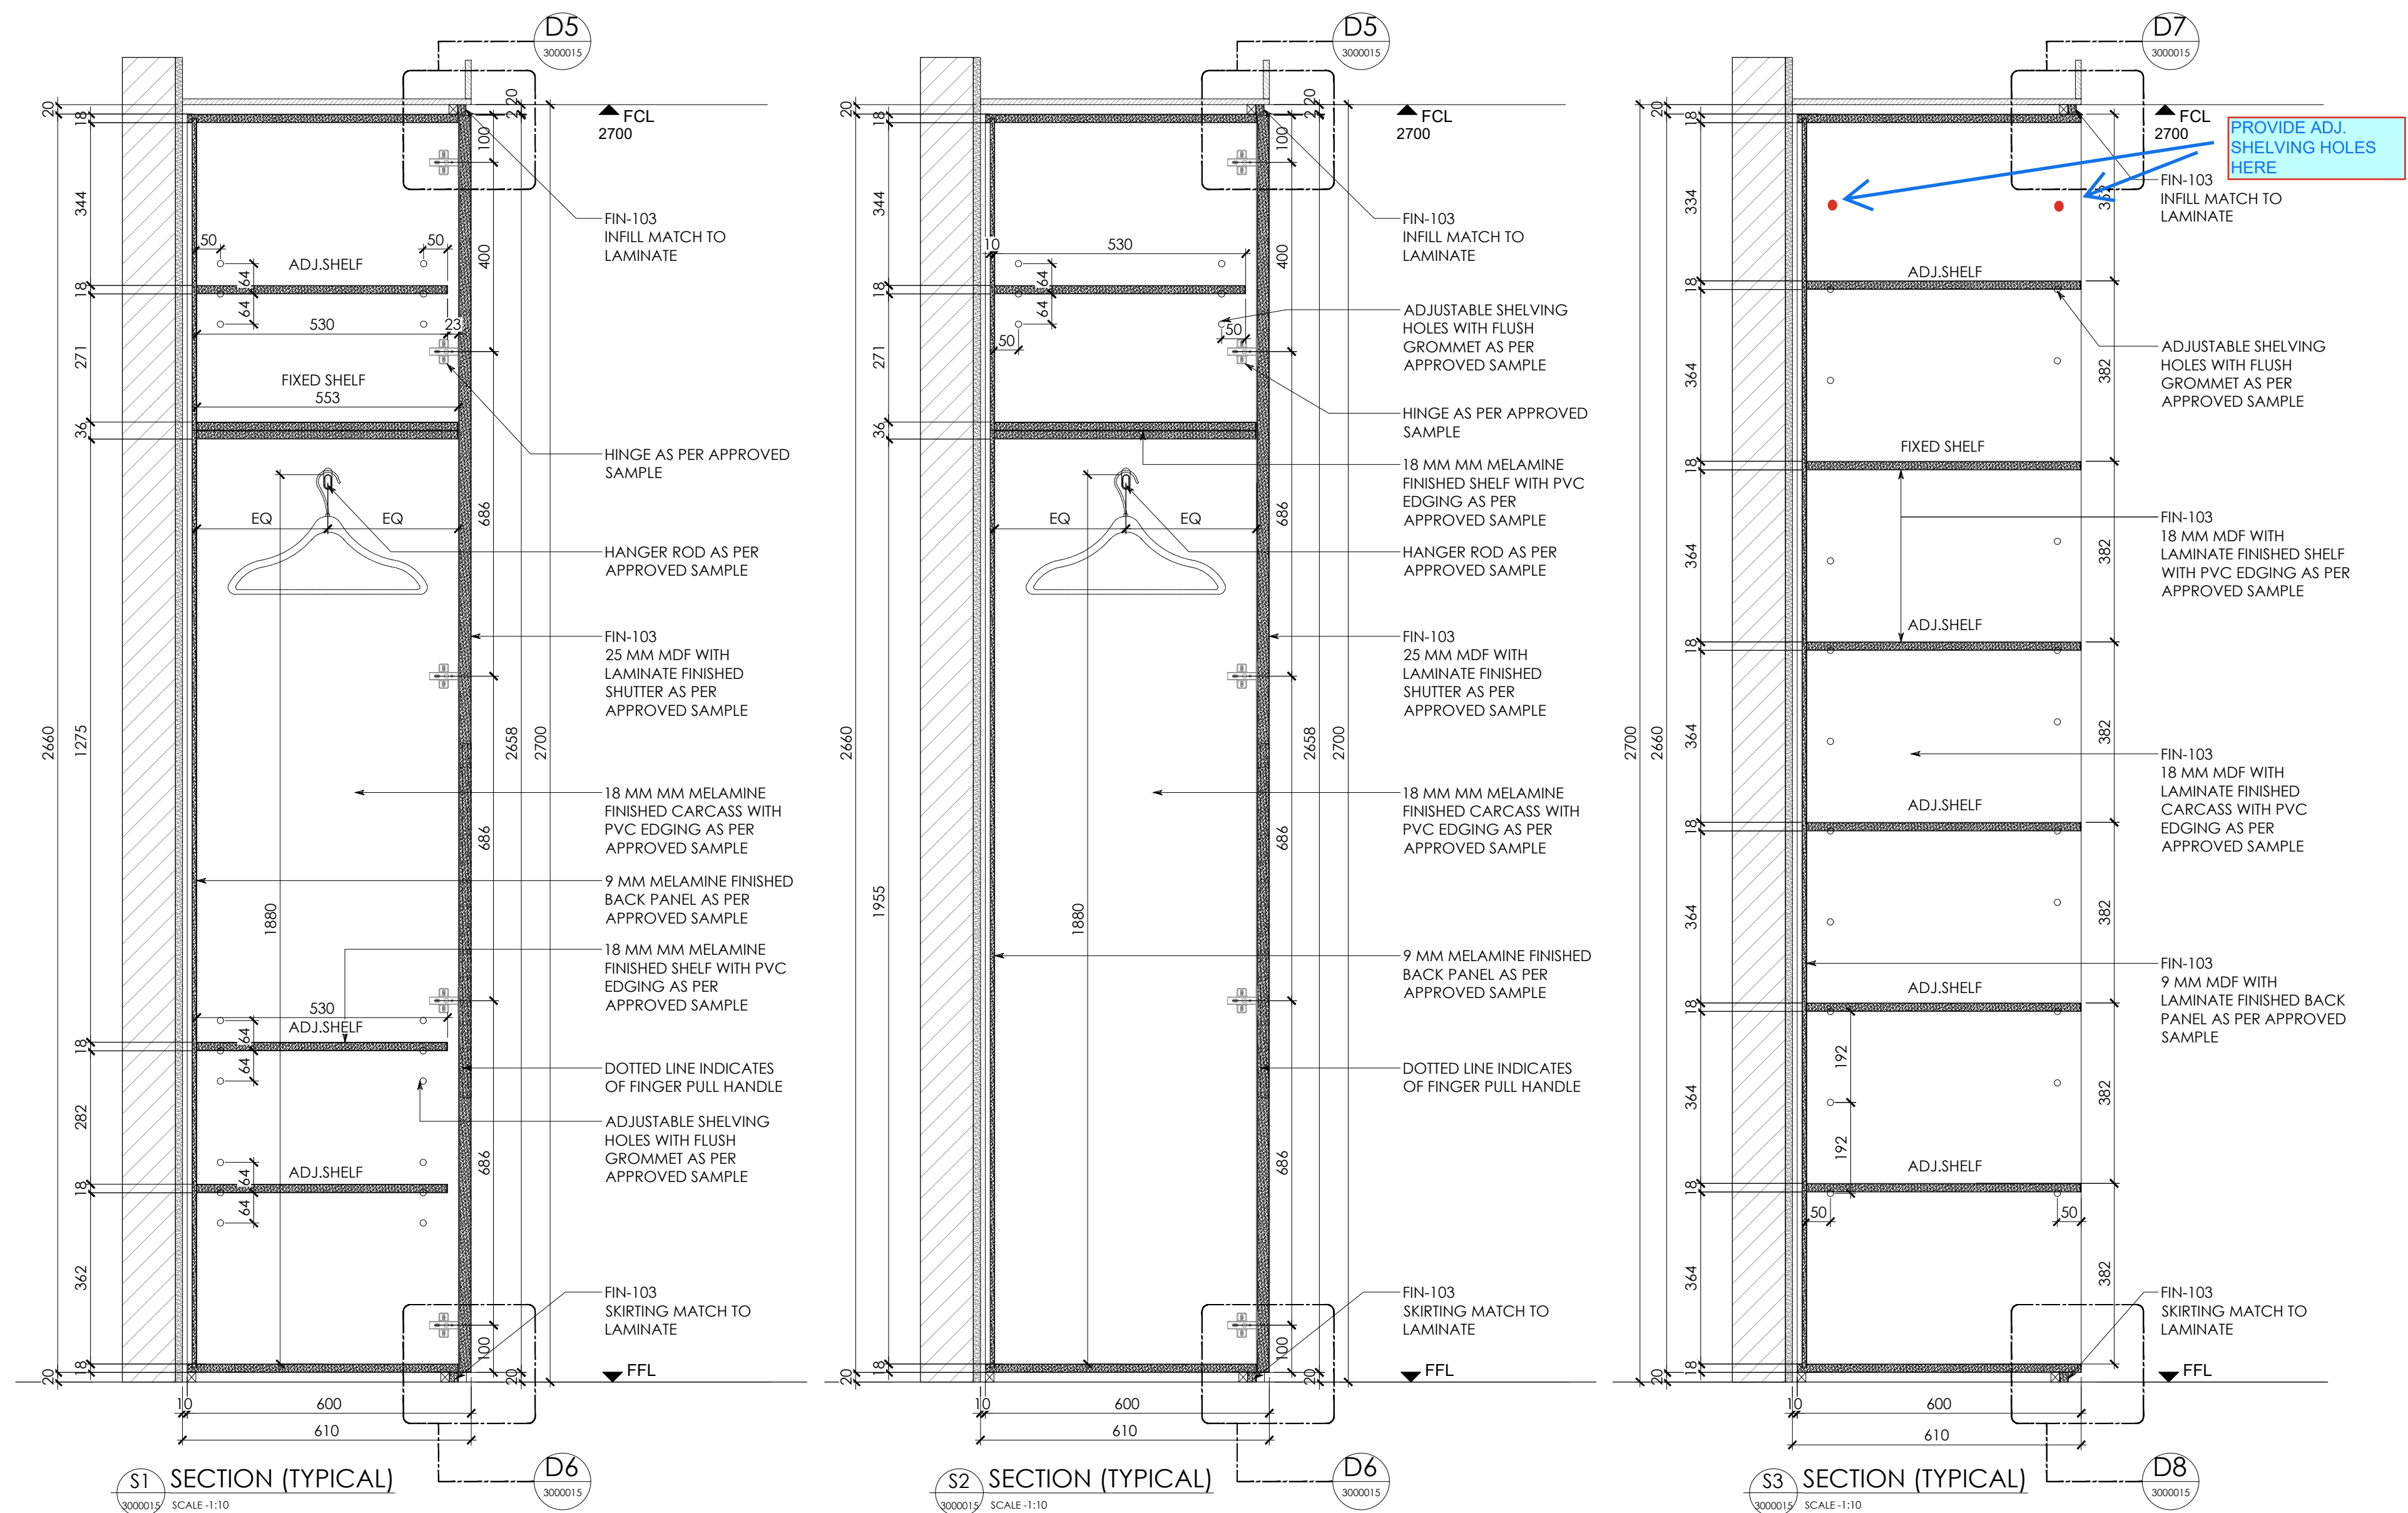


DAE:
1. TO BE COORDINATED WITH IFC DRAWINGS/ SPEC'S/ SCHEDULES
2. WIDTH/ DEPTH/ HEIGH OF WARDROBES TO CONFORM WITH IFC ARCH PLANS AND APARTMENT WARDROBE AND CABINET SCHEDULE C3079-SCH-2TR5600-AR-000007(A) FOR ALL BUILDINGS
3. CONDUCT/ VERIFY FIELD MEASUREMENTS PRIOR TO PROCEEDING ANY FABRICATION
4. ALL DOOR FRONT/BACK/SIDES/ EDGES ARE TO BE FIN-103
5. SUBMIT MELAMINE FACE SAMPLE OF CARCASS FOR SEPERATE APPROVAL; PROVIDE SIMILAR/ APPROXIMATE FINISH FIN-103
6. SUBMIT FIN-103 SAMPLE, HINGES, HARDWARE, HANGER ROD FOR SEPERATE CLIENT APPROVAL

Copyright by Expo City Dubai. All rights reserved. This document may not, in whole or in part, be reproduced, stored, transmitted or distributed in any form or by any means, whether electronic, mechanical, by photocopy, recording or otherwise, without the prior written permission of Expo City Dubai. Except where otherwise expressly agreed in writing by Expo City Dubai, Expo City Dubai shall have no responsibility or liability for any loss (direct, consequential or otherwise) which may arise from reliance on or use of this document or the information contained therein.
DO NOT SCALE THIS DRAWING.

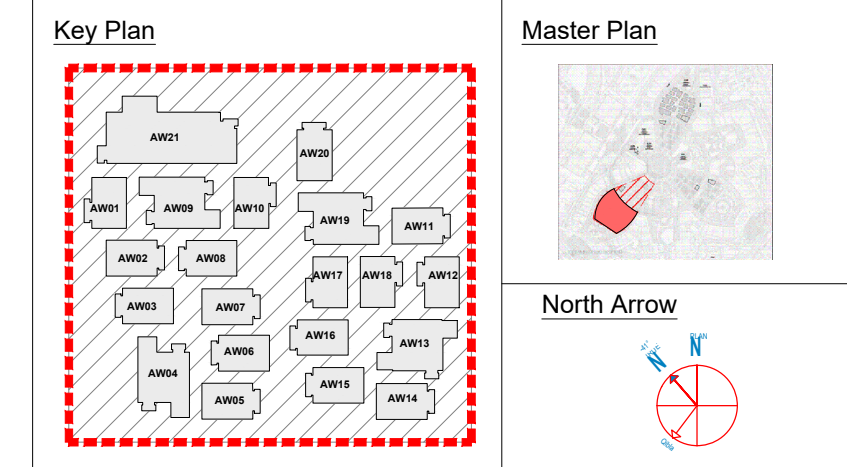

General Notes

REFERENCE-IFC
01 WARDROBE TYPICAL DETAILS -C3079-DWG-2TR5600-AR-4002001
02 WARDROBE TYPICAL DETAILS -C3079-DWG-2TR5600-AR-4002002

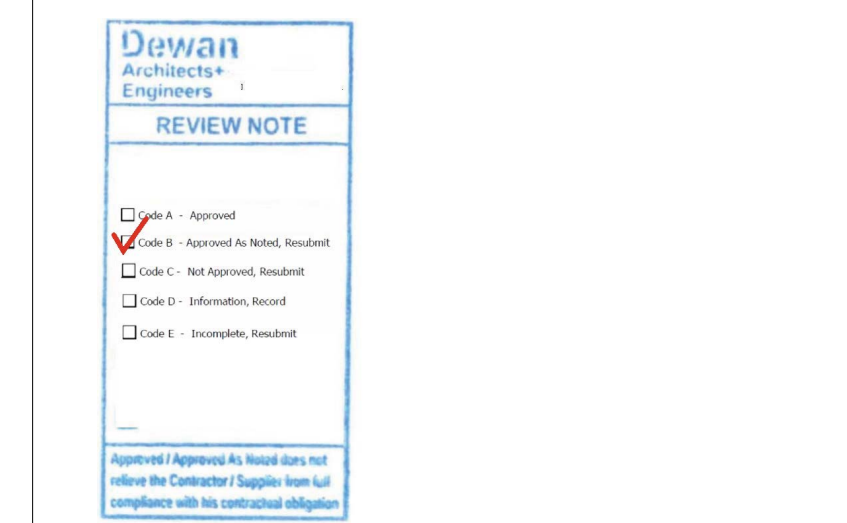

No	Description
1	
2	
SAFETY, HEALTH AND ENVIRONMENT INFORMATION
Brief details on the identified hazard symbol referencing the unusual residual hazards / risks are listed above.

Rev	Description	Drawn	Apvr	Chk'd	Date
1	FIRST ISSUE	BNB	KABILAN	RAJA	07-03-2026

Client

مدينة إكسبو دبي
EXPO CITY DUBAI

Design Consultant
HOPKINS ARCHITECTS

Supervision Consultant
Dewan Architects + Engineers

Main Contractor
ARCO GROUP
P.O.Box: 5430 | Dubai, United Arab Emirates | Tel: +971 4 2677603 | Fax: +971 4 2677604
E-mail: info@arccogroup.org | Website: www.arccogroup.org

Project Title
AL WAHA RESIDENCE 01
EXPO CITY DUBAI

Drawing Title

PHASE-01 - MOBILITY DISTRICT
TYPICAL WARDROBE SECTION AND SPORT
DETAILS FOR BUILDING AW1 TO AW21
SHEET (01/01)

Approved
KABILAN
Seal Date
07-03-2026

Designed
DESIGNED BY
Drawn
BNB
Checked
RAJA
Model File Ref:
Scale A1(594x841)
Revision No
AS SHOWN
1

Drawing No
C5128-SDW-2TR5600-FO-3000015